

ZGSZ/SZX



JEPPESSEN

SHENZHEN, PR OF CHINA

9 MAY 25

10-8


Eff 14 May 1600Z

BAOAN


TEMPORARY CHART - CONSTRUCTION WORKS

REFER ALSO TO LATEST NOTAMS

New RWY and TWYs are under construction.
Excercise caution while landing, taking off and taxiing.

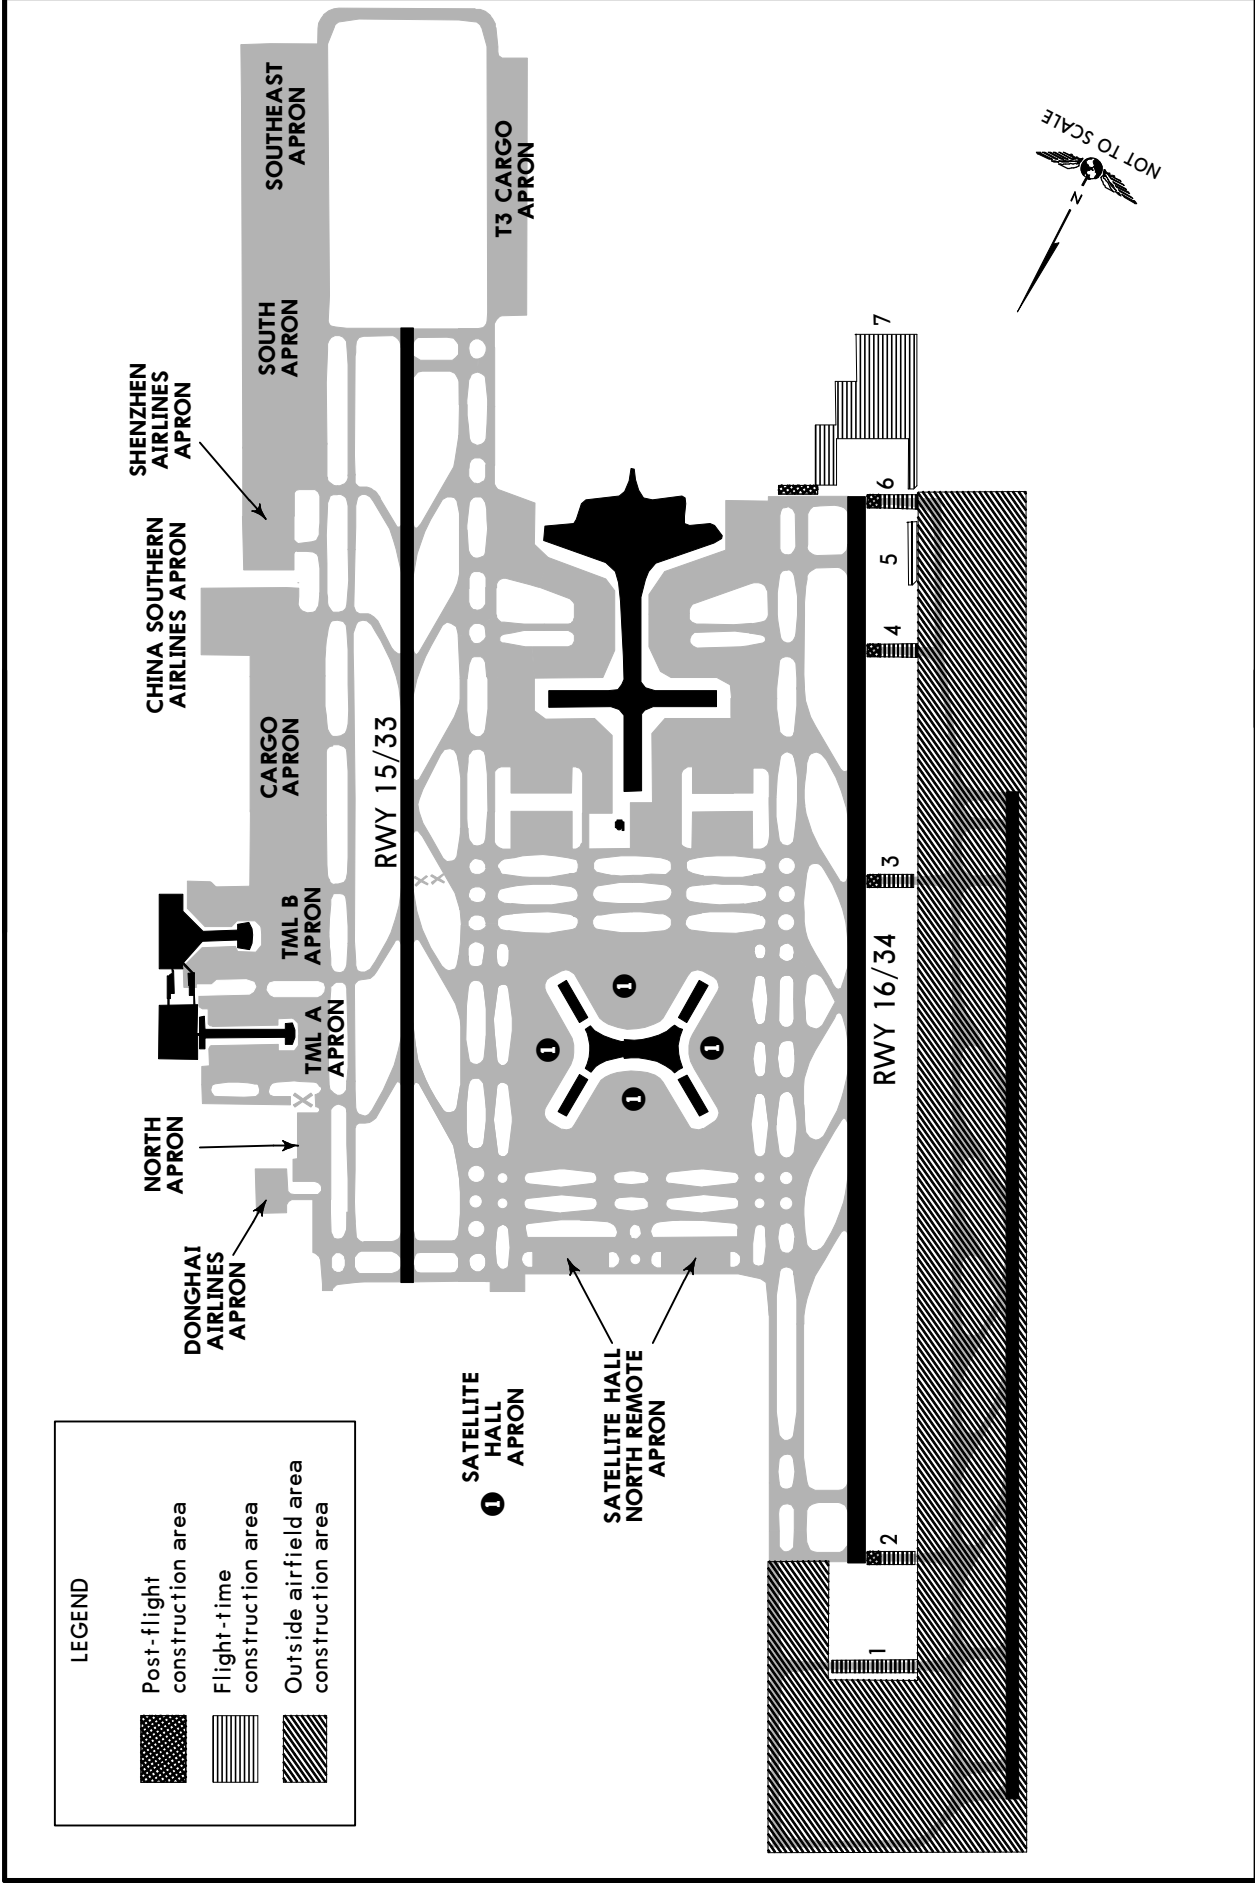


CHANGE	D-ATIS 127.45	ACARS: D-ATIS	*BAOAN Delivery	*BAOAN Ground		Apron			Tower	
	(Chinese 126.85)	*PDC *DCL	121.95	West 121.8	East 121.65	APN01 122.7	APN02 121.625	APN03 122.825	West (Rwy 16/34) 118.45	East (Rwy 15/33) 130.35

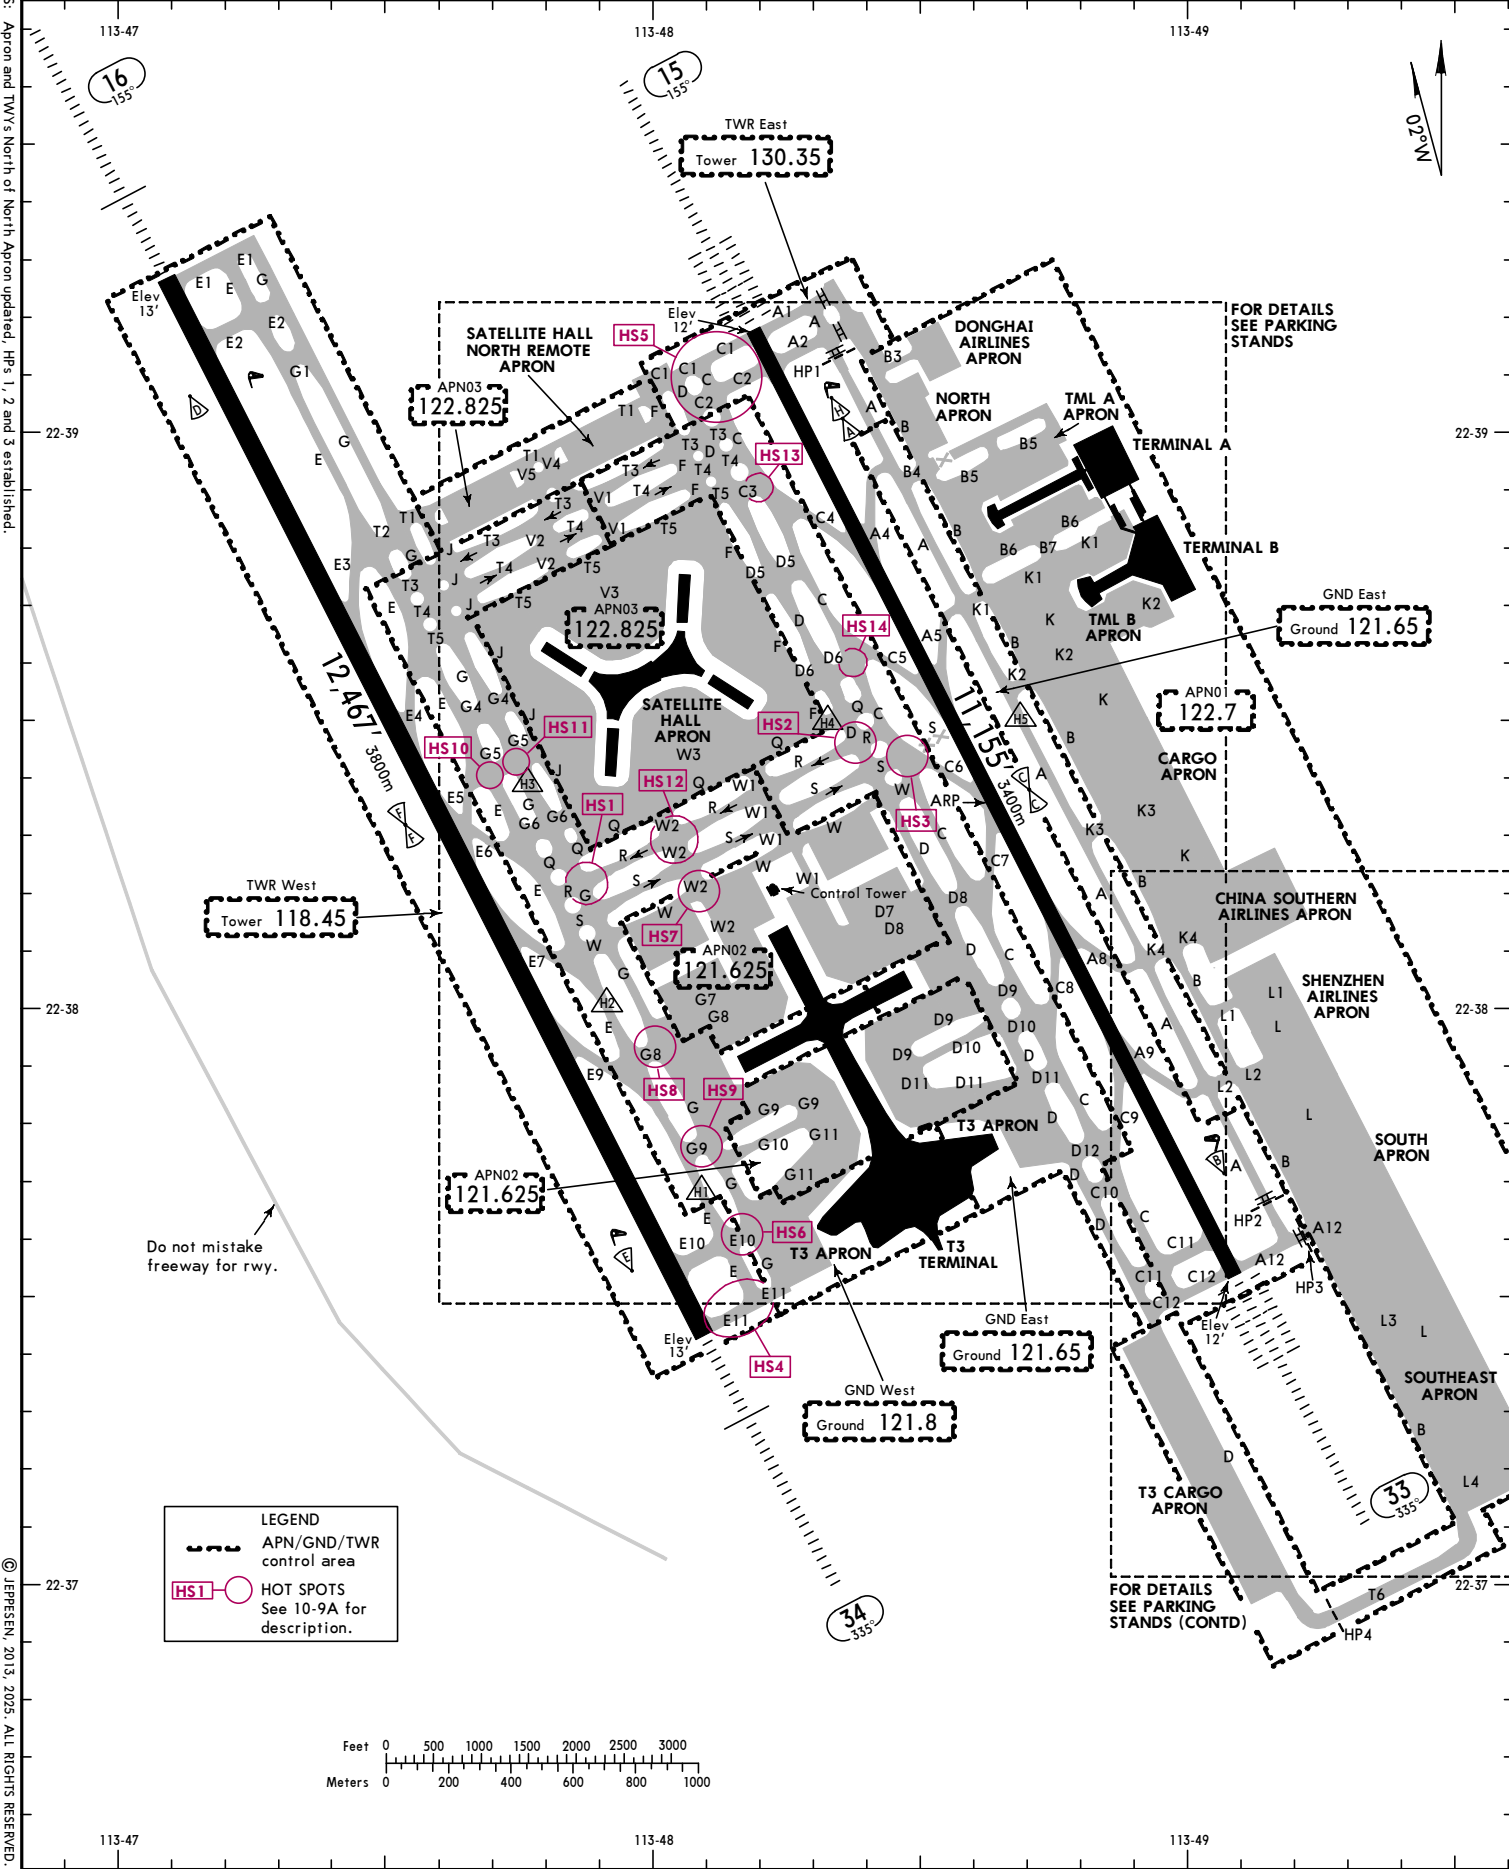

CHANGES: Apron and TWR's North of North Apron updated; HP 1 established.

© JEPPESEN, 2013, 2025. ALL RIGHTS RESERVED.

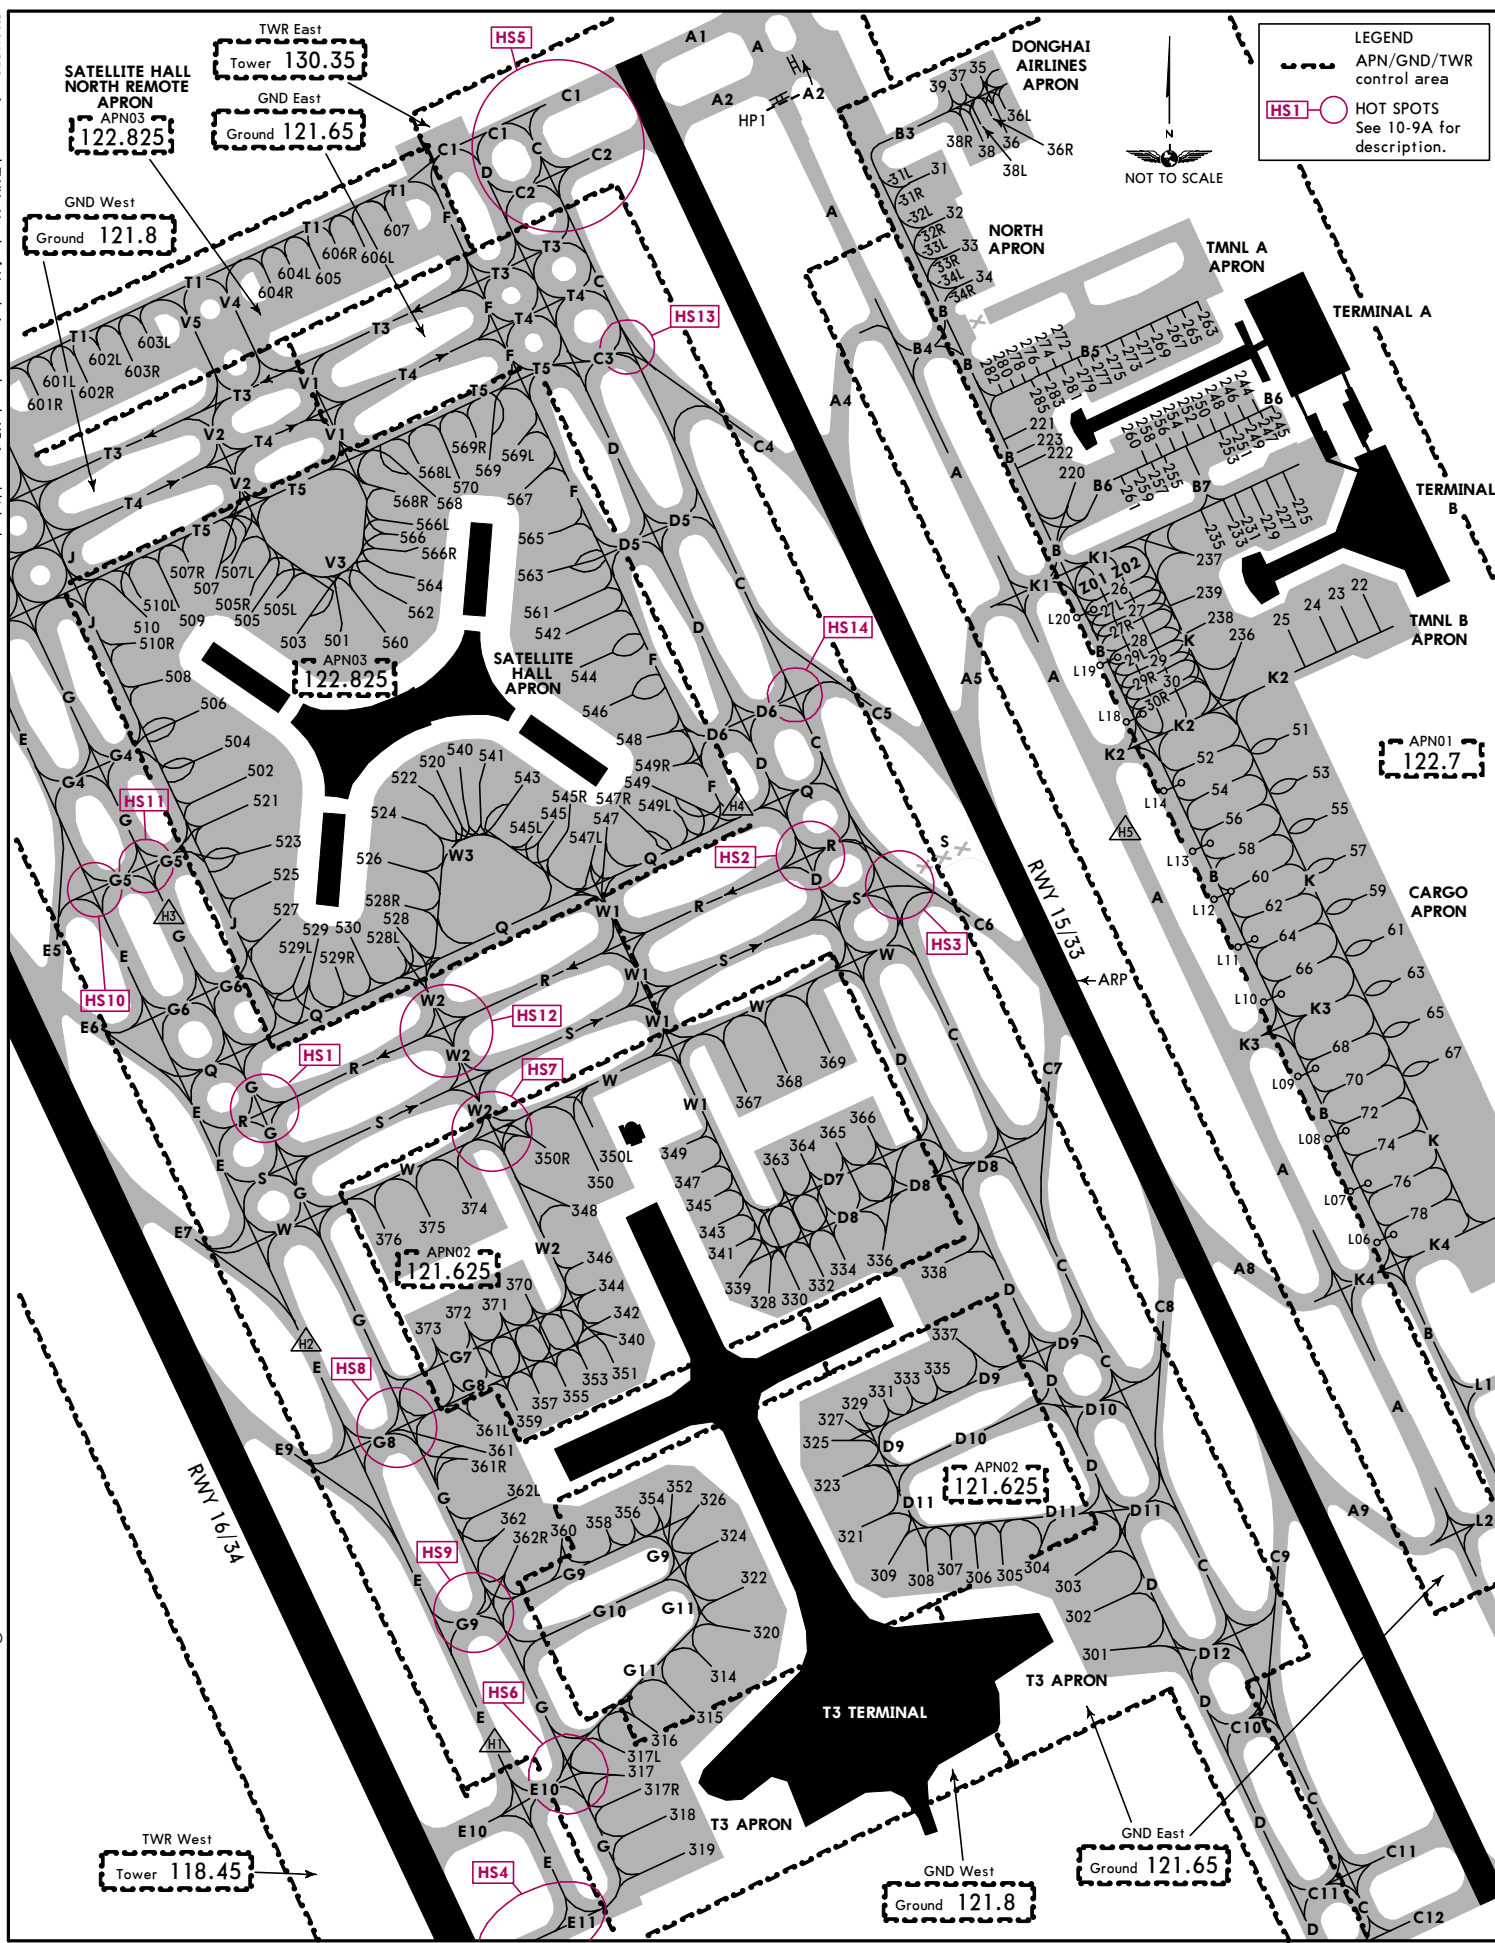


ZGSZ/SZX

JEPPESEN SHENZHEN, PR OF CHINA
9 MAY 25 10-9B EFF 14 MAY 1600Z
BAOAN

ZGSZ/SZX

JEPPesen SHENZHEN, PR OF CHINA
9 MAY 25 **10-9C** Eff 14 May 1600Z
BAOAN

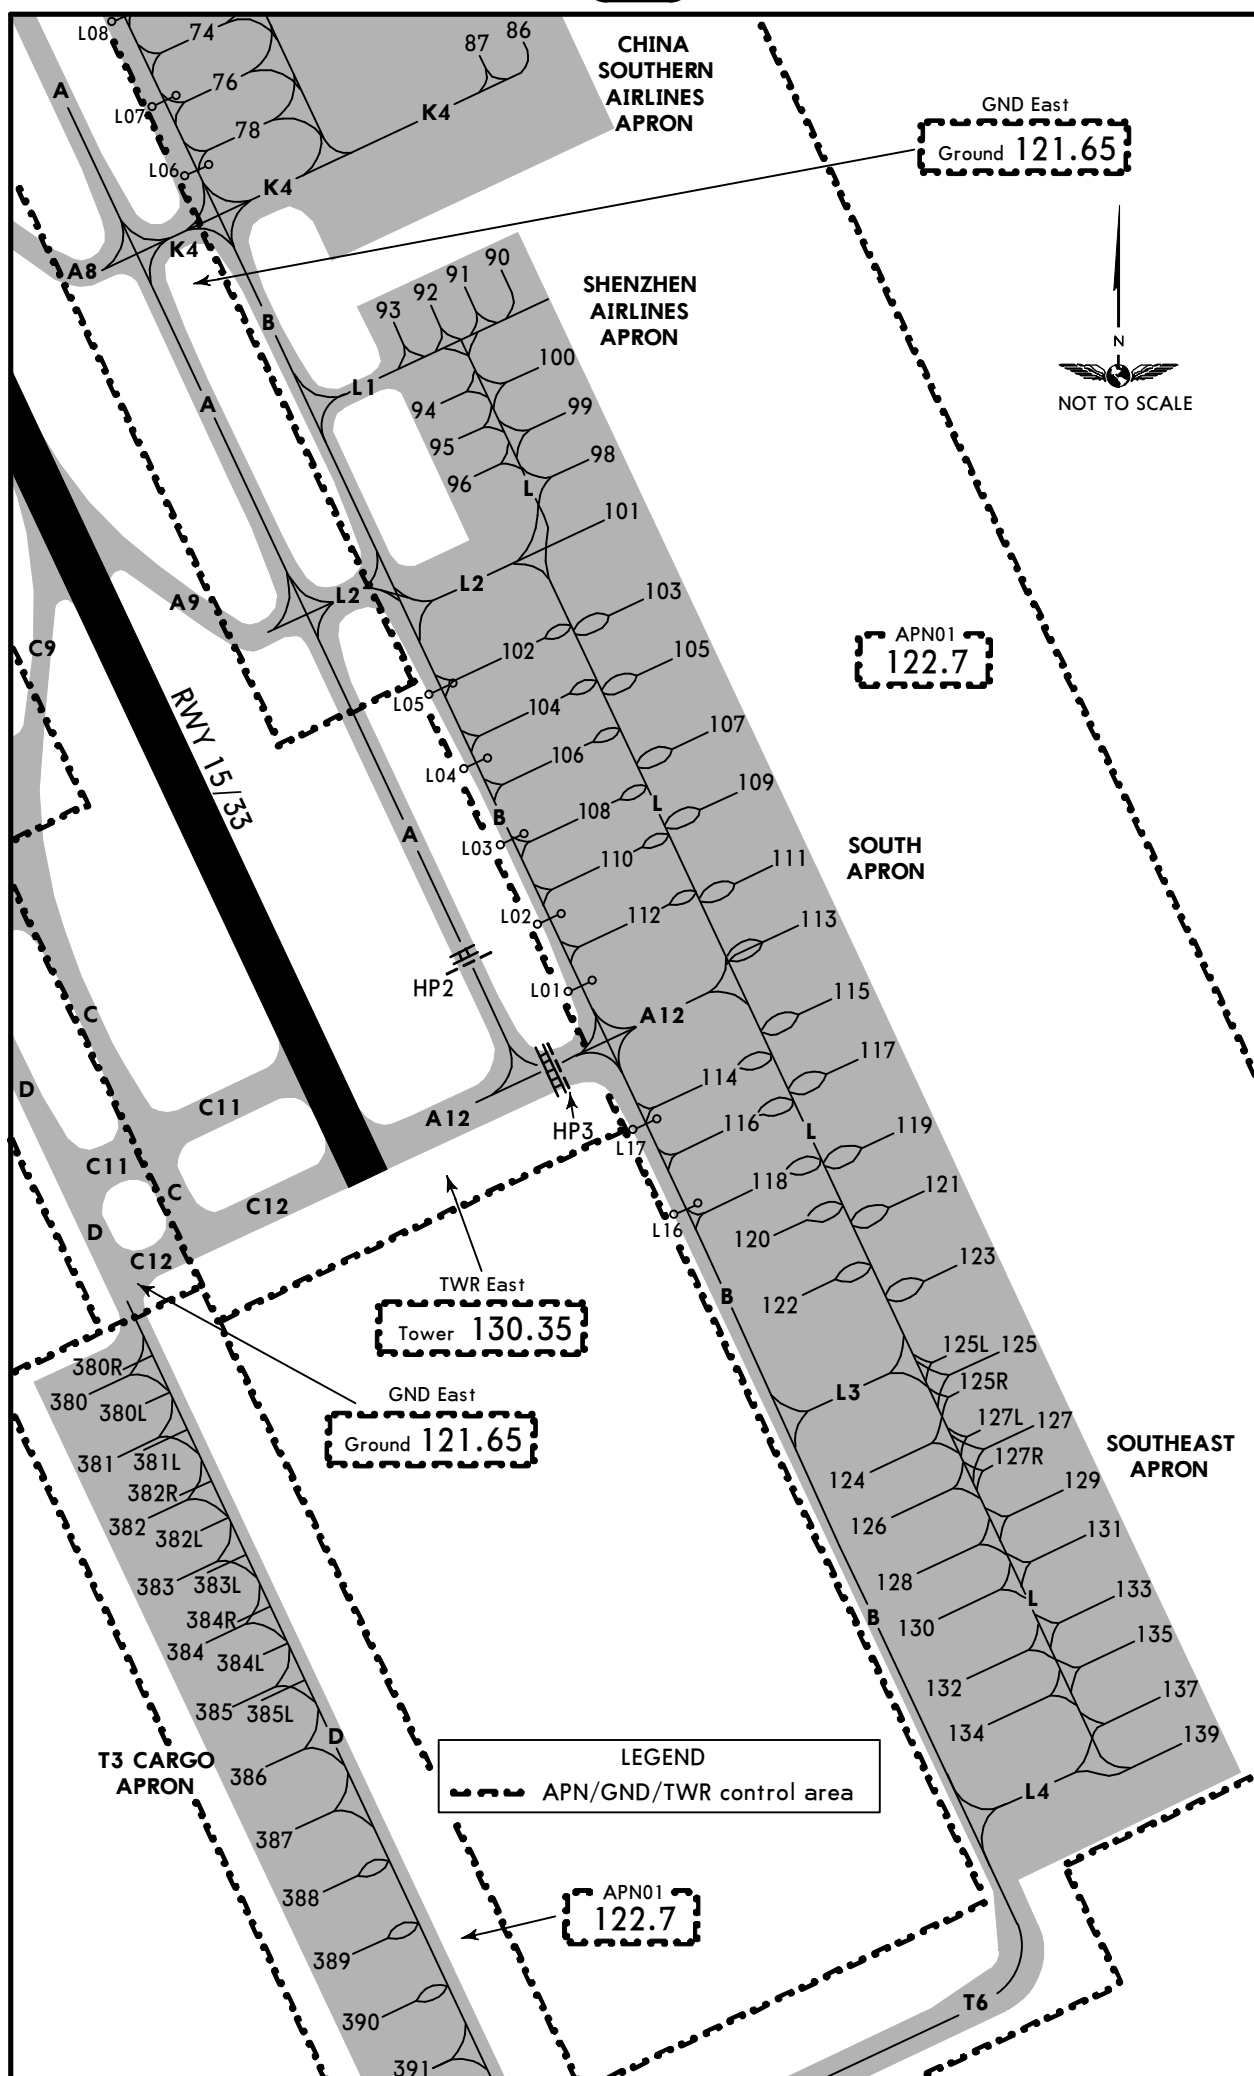

CHANGES: HPs 2 and 3 established.

© JEPPesen, 2017, 2025. ALL RIGHTS RESERVED.